


Aminata

Bah


Architecture
portfolio

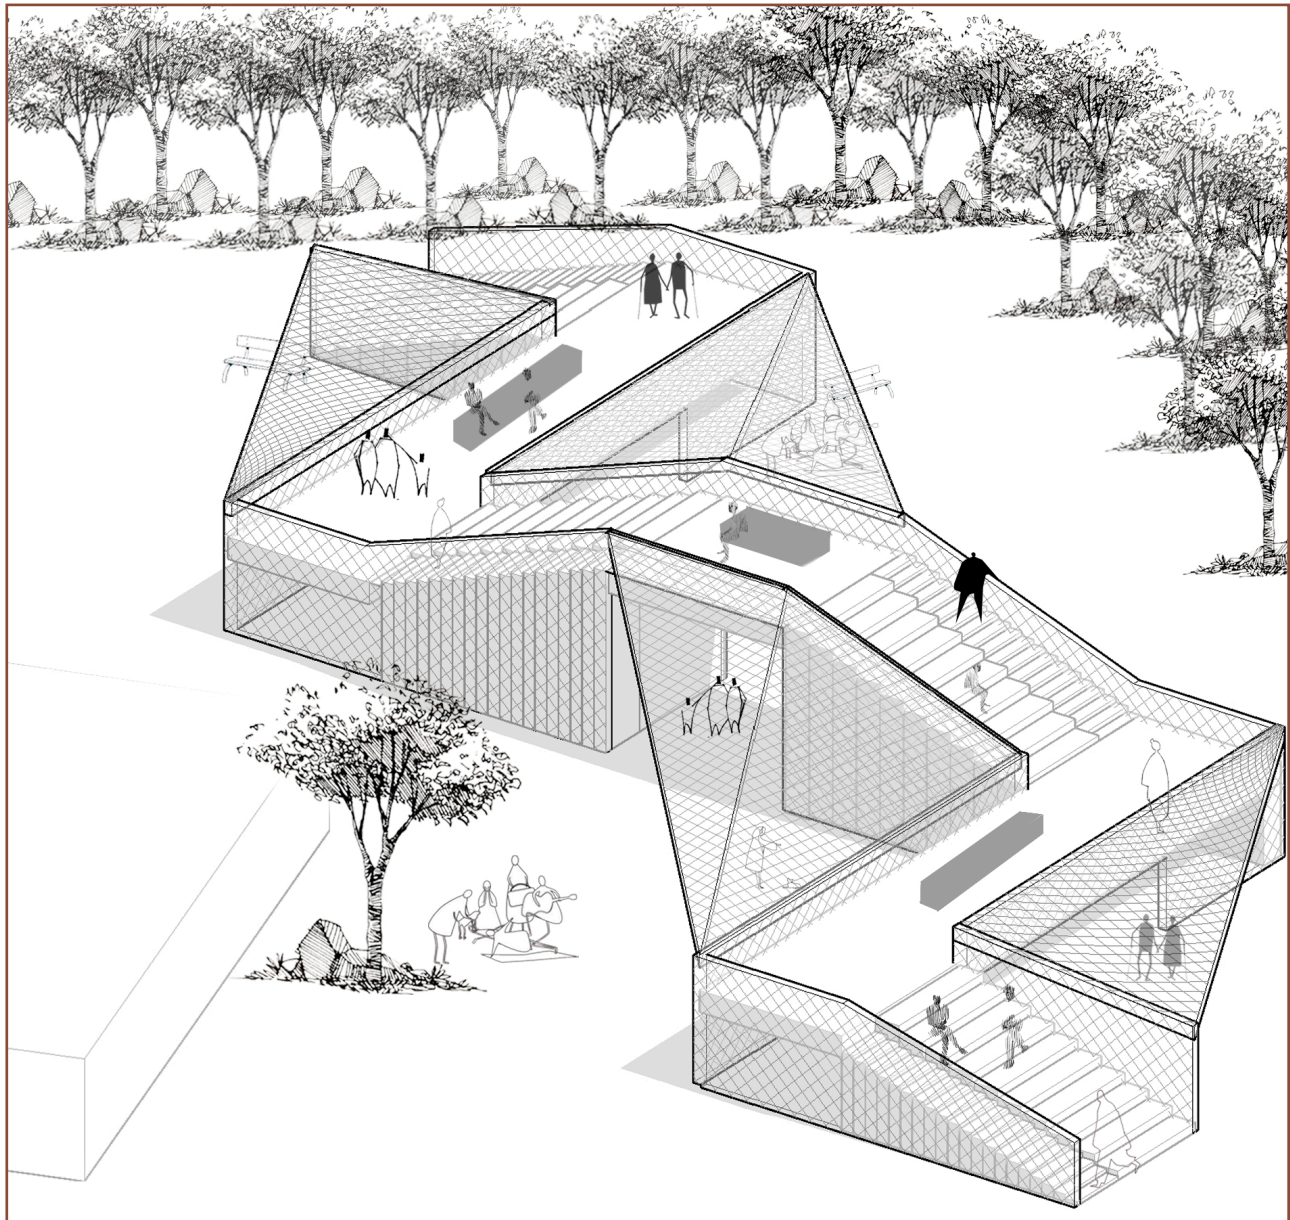

Contents

01	Aviary	pp3-10
02	Mill Street Pavilion	pp11-18
03	Modern winery	pp19-24
04	Other work	pp25-28



01 Aviary
Chicago IL

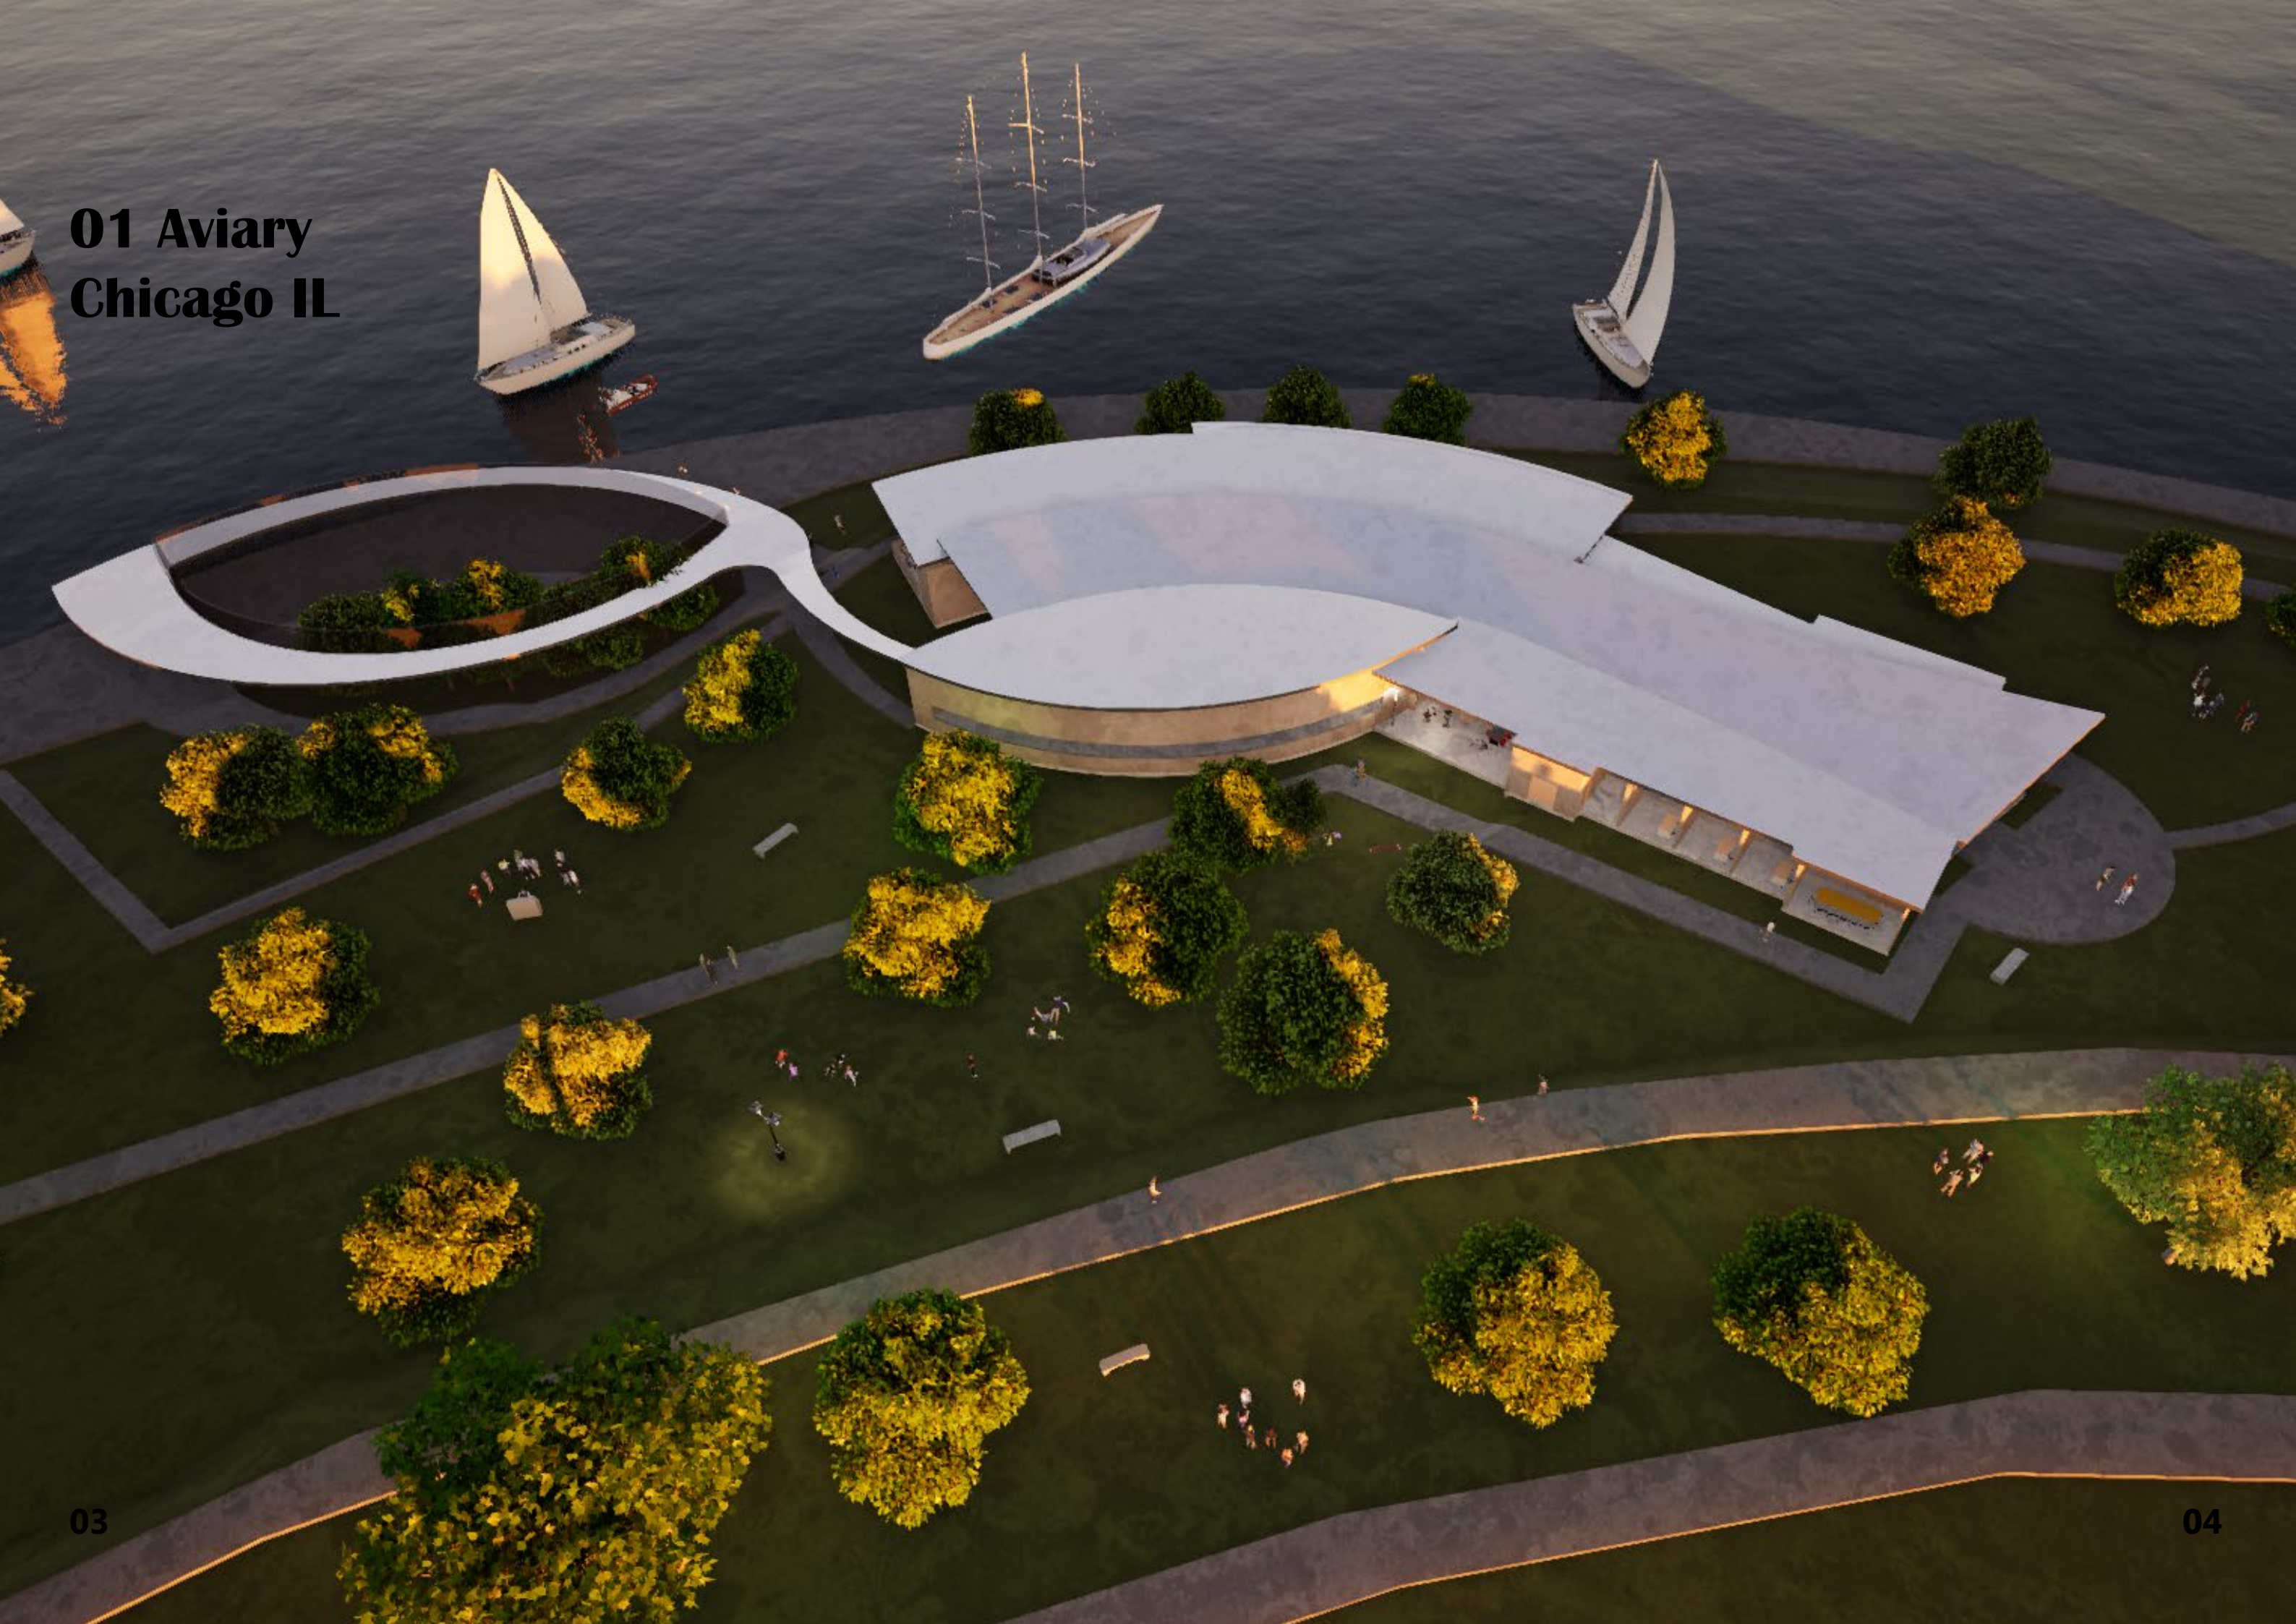


Lake shore drive

Aviary

This project proposes an aviary designed to create a safe and supportive environment for migratory birds throughout the year, with particular focus on Chicago's seasonal migration periods. The aviary functions as a resting and recovery space for multiple bird species, offering a habitat that feels familiar and secure. By providing an alternative refuge within the urban landscape, the design helps reduce bird collisions with the glass façades of surrounding skyscrapers while fostering coexistence between wildlife and the city.

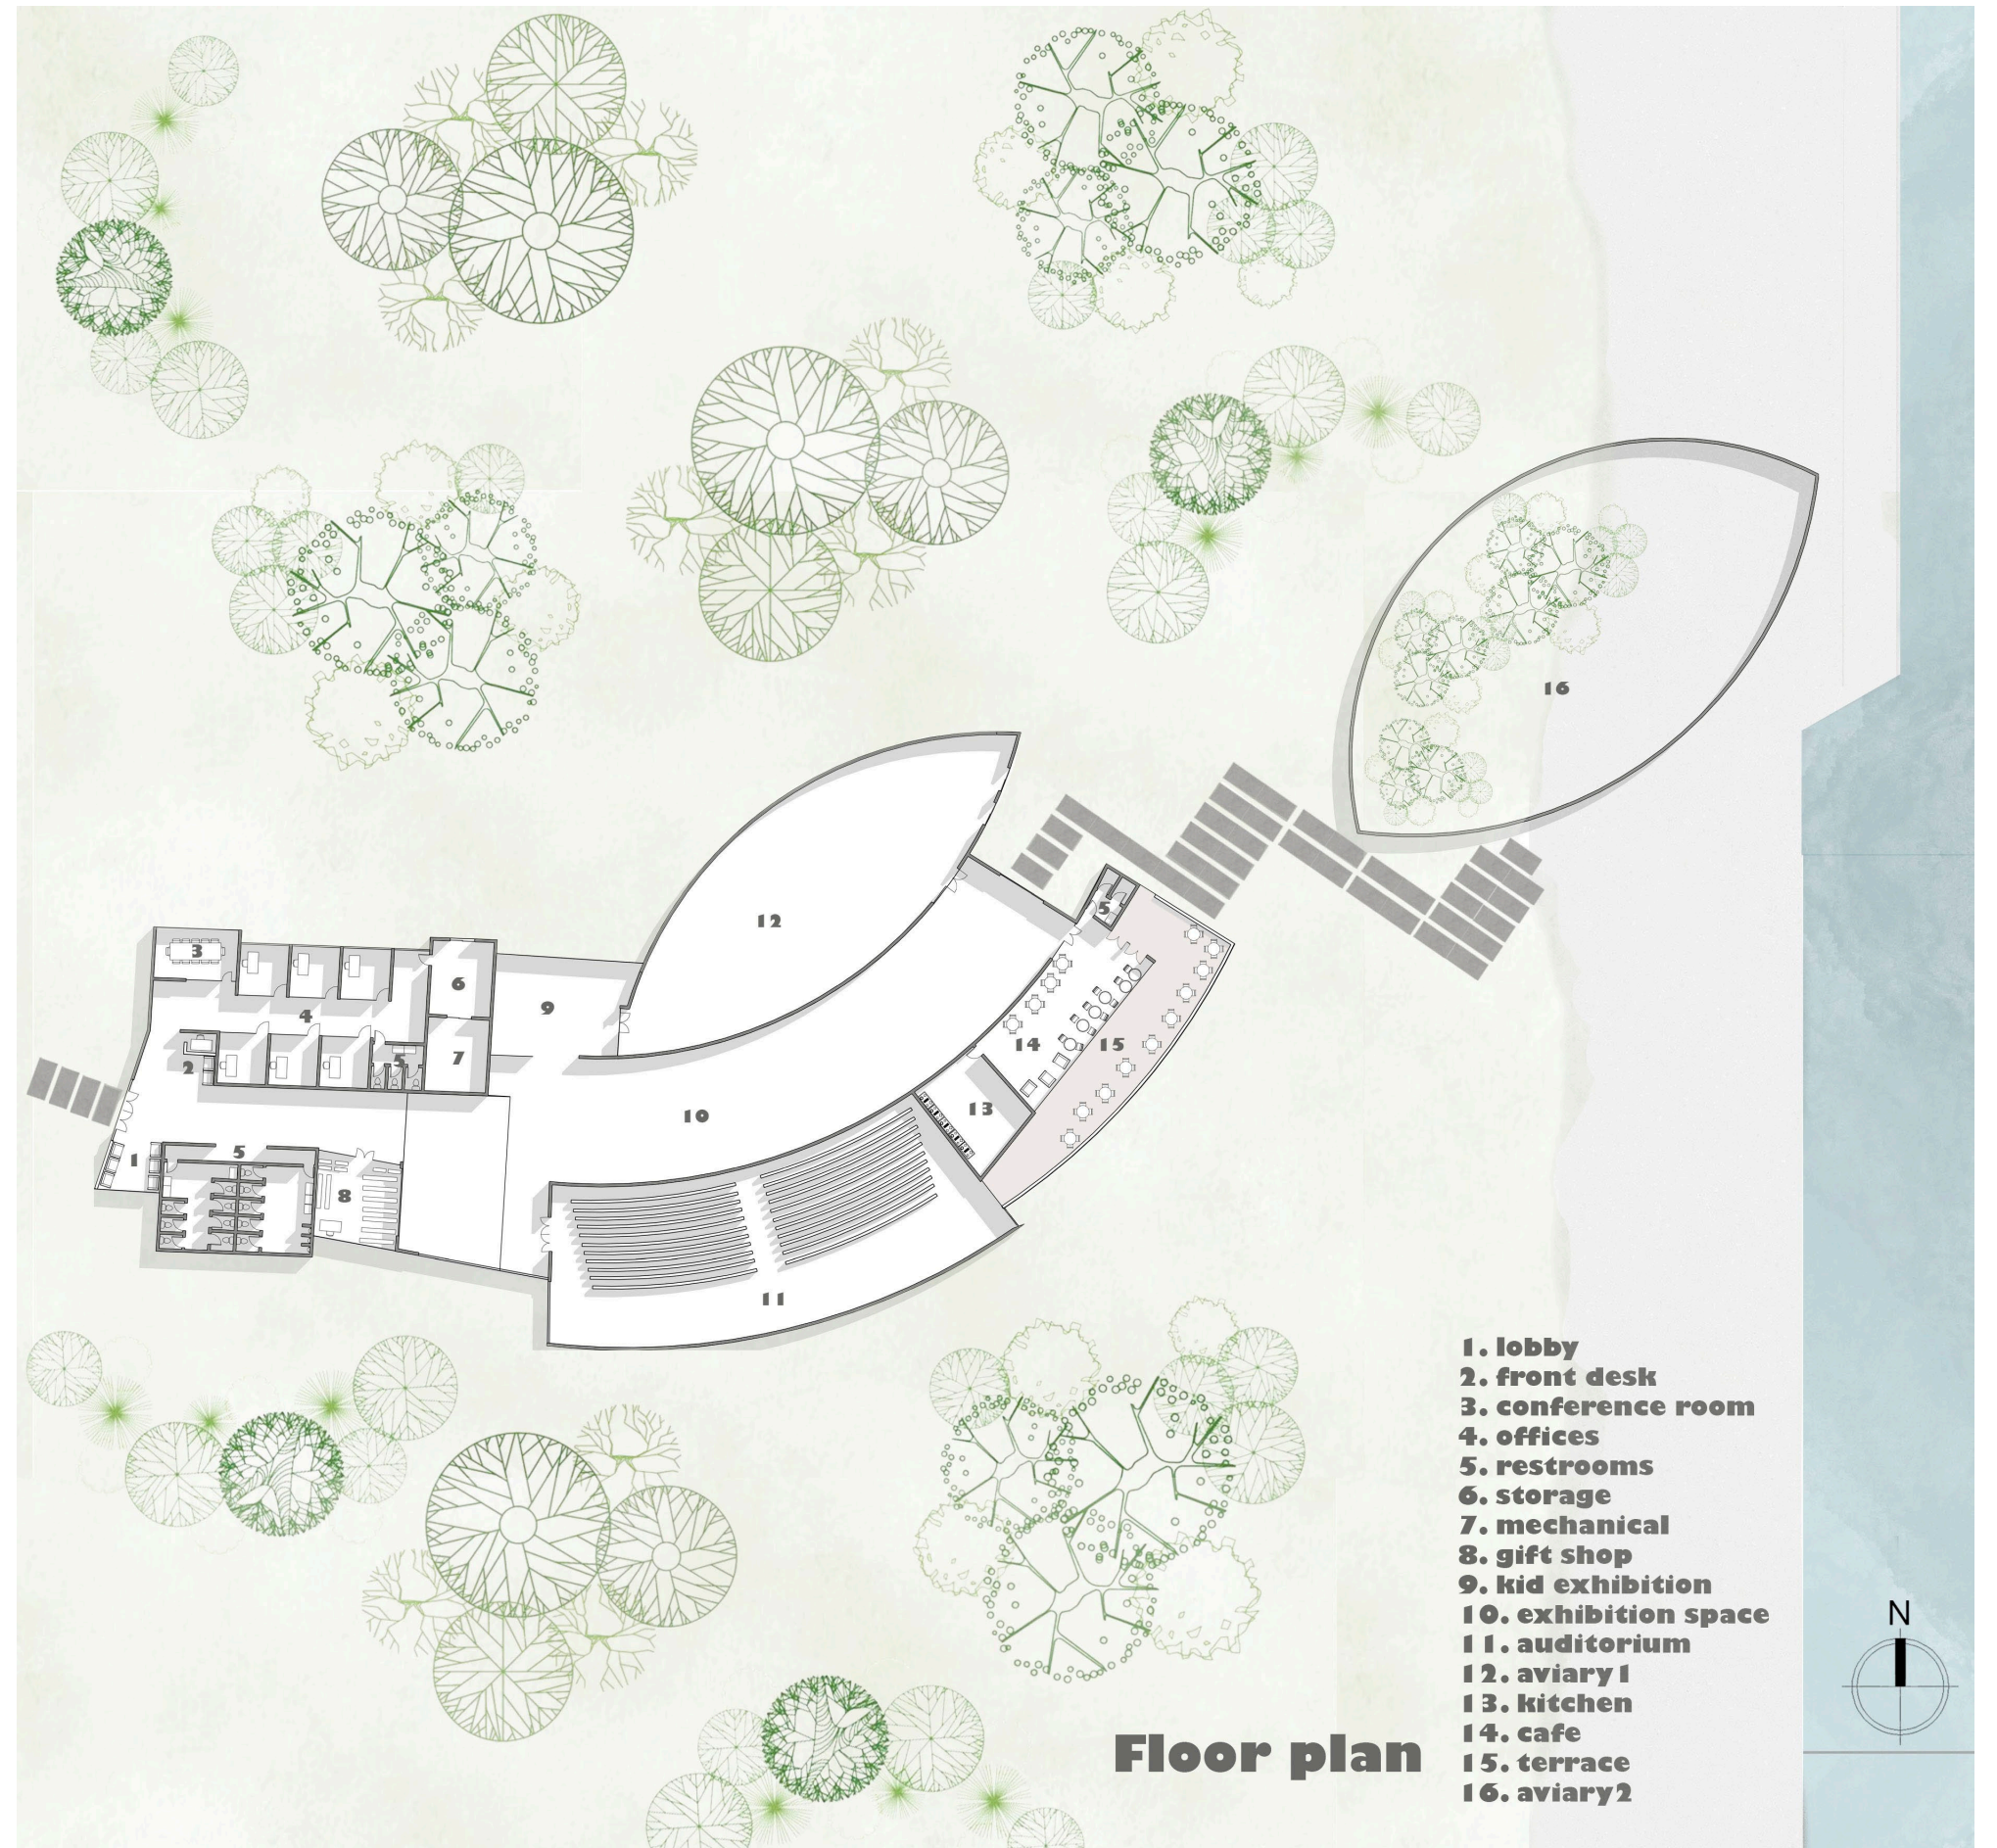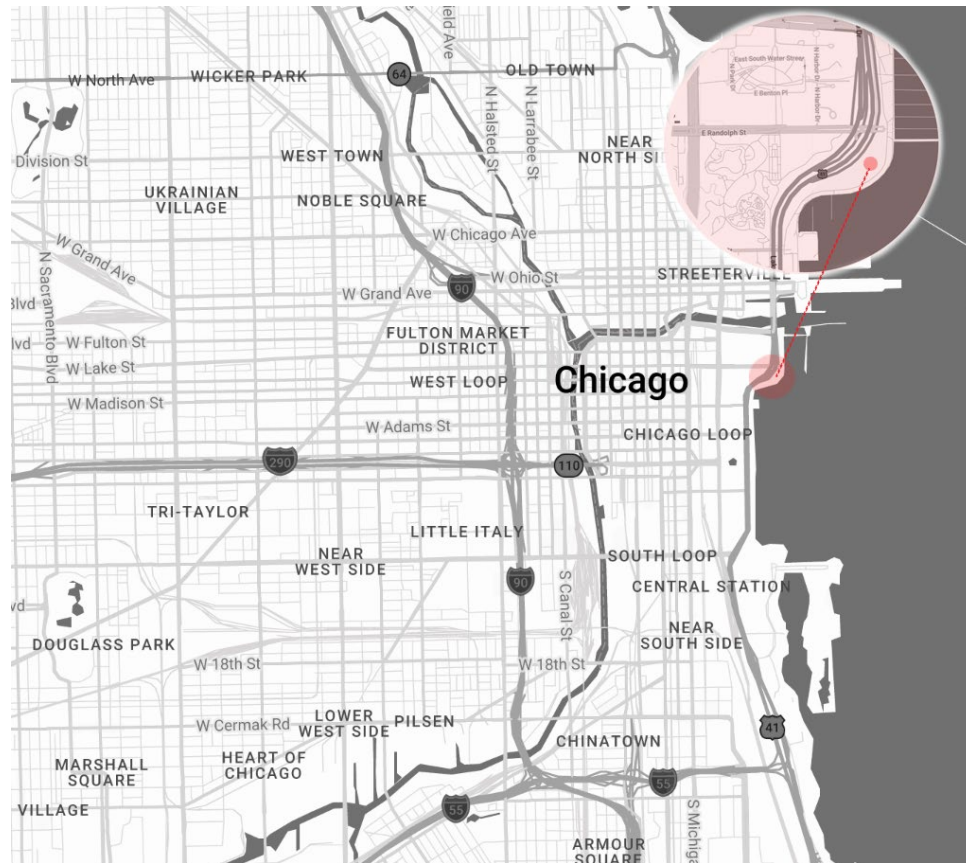

South Elevation

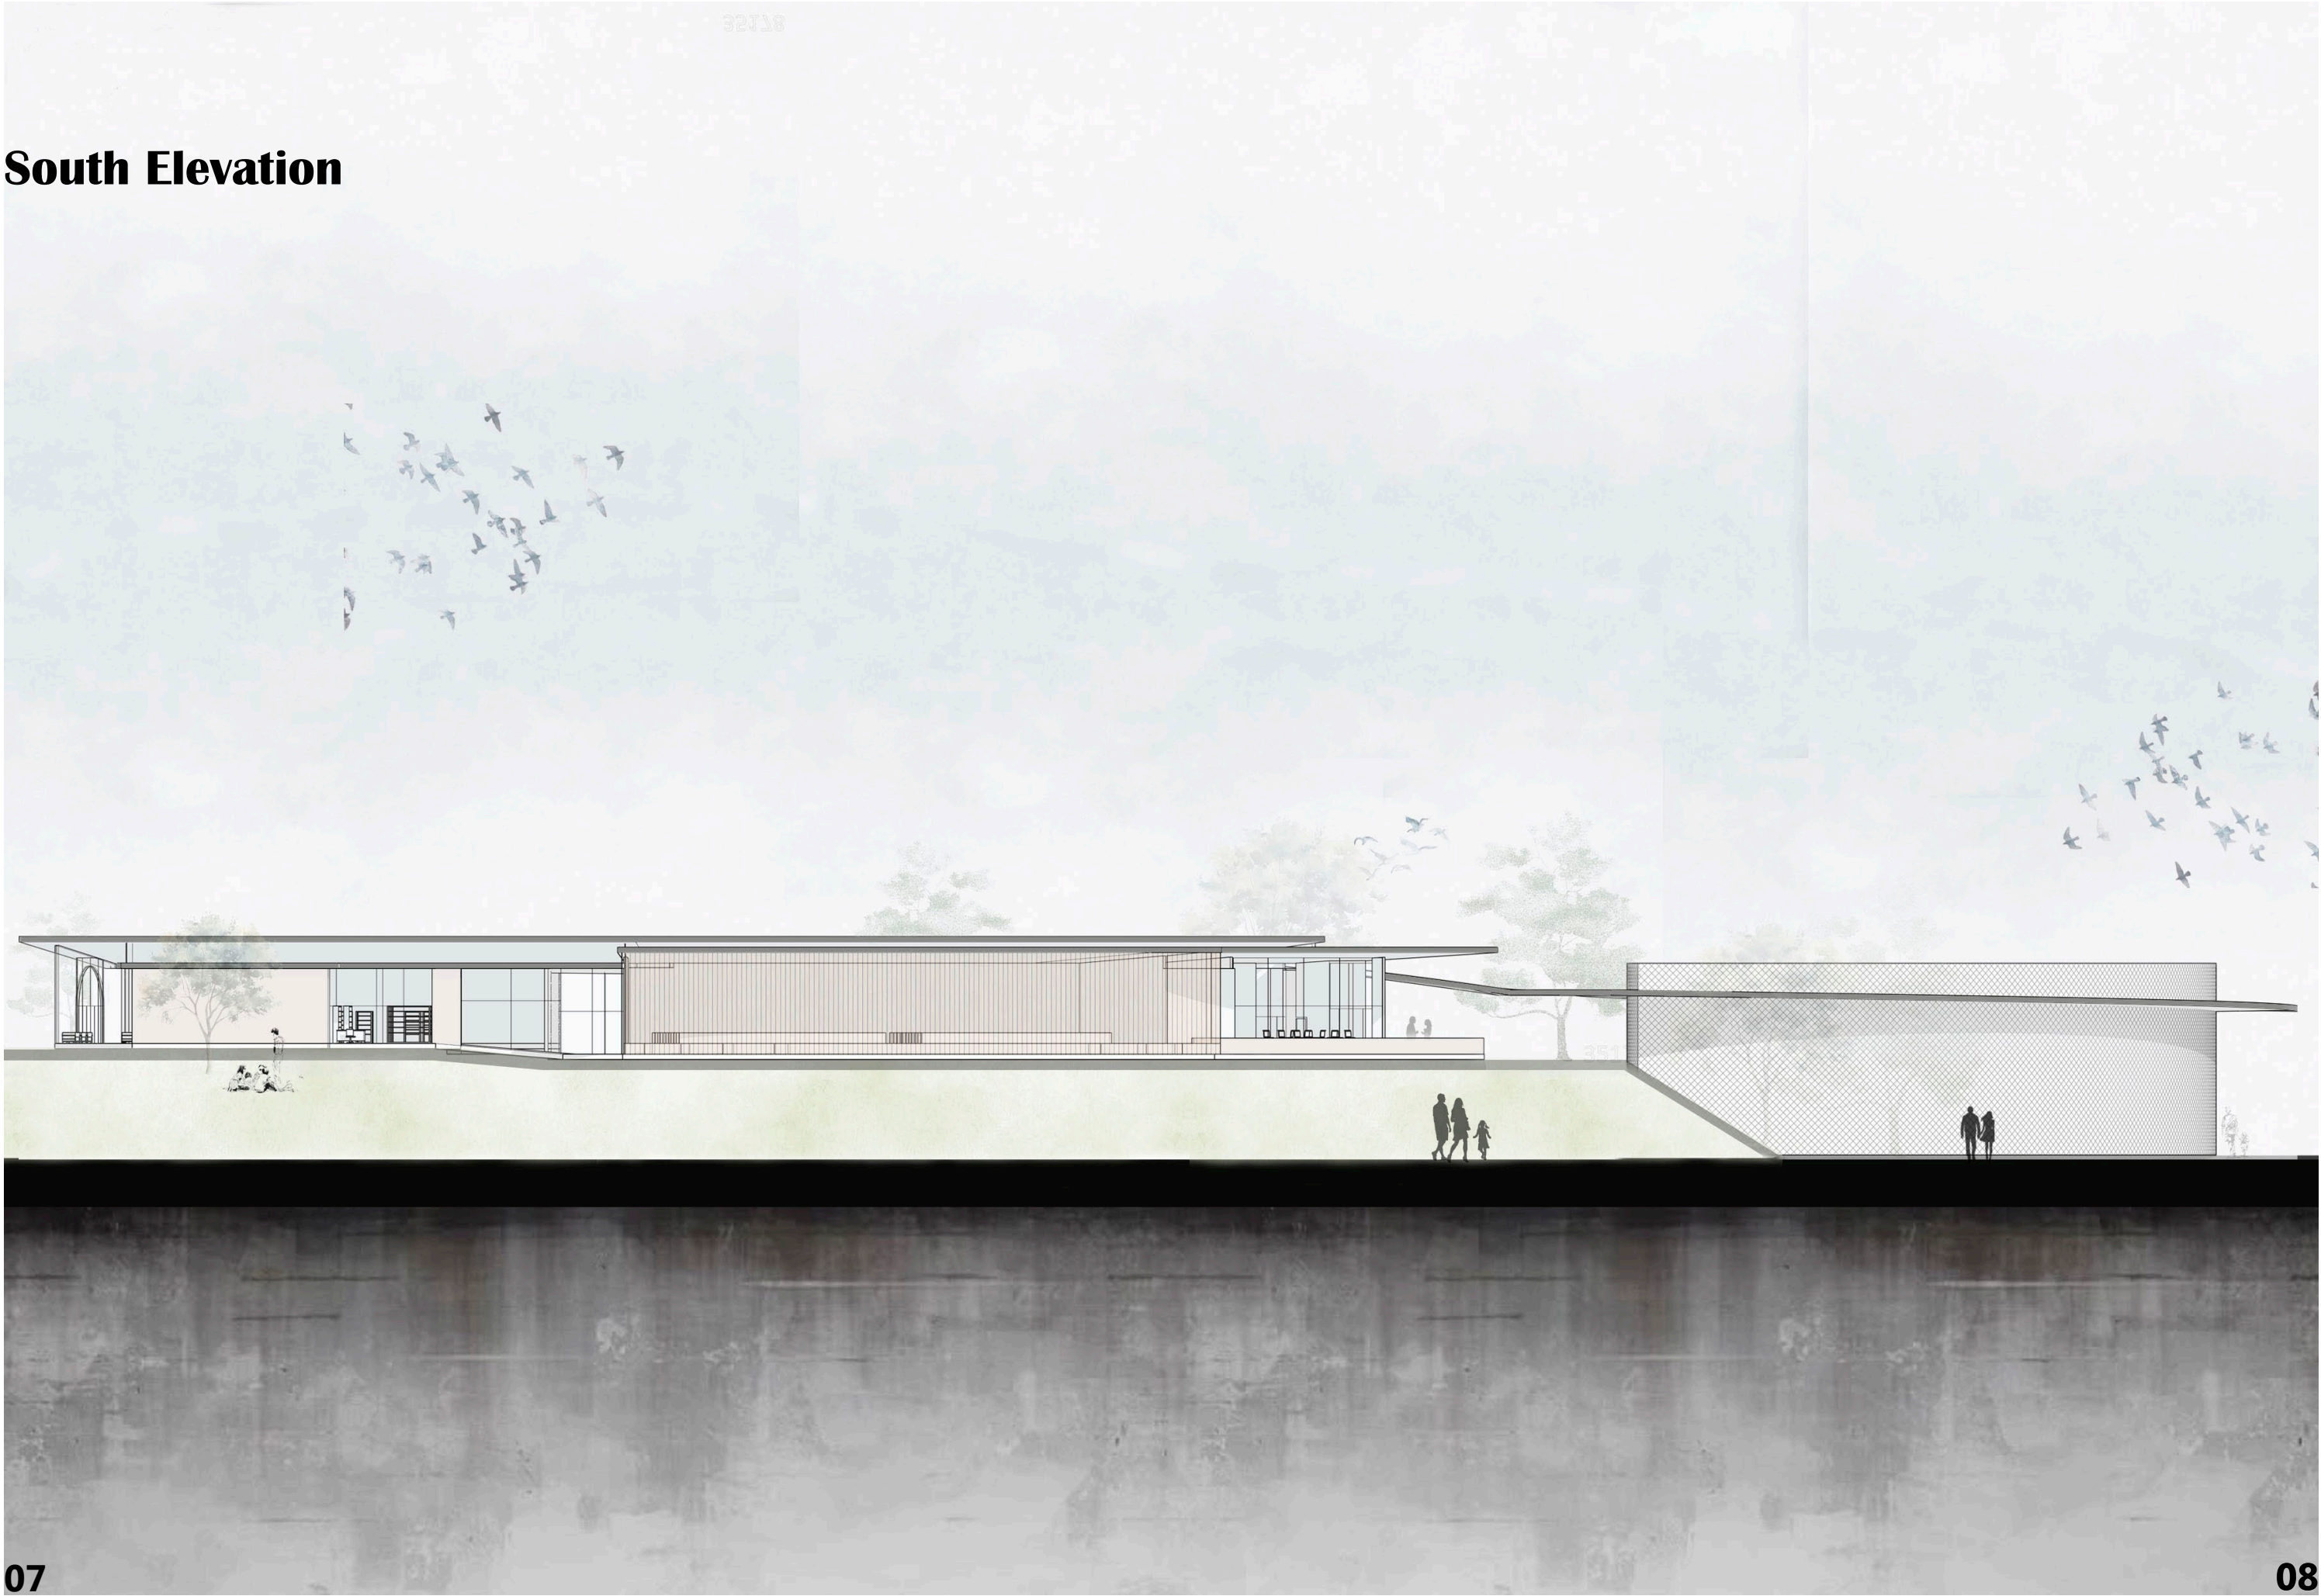




Exhibition space



Cafe


02 Mill Street Pavilion
Springfield Mo

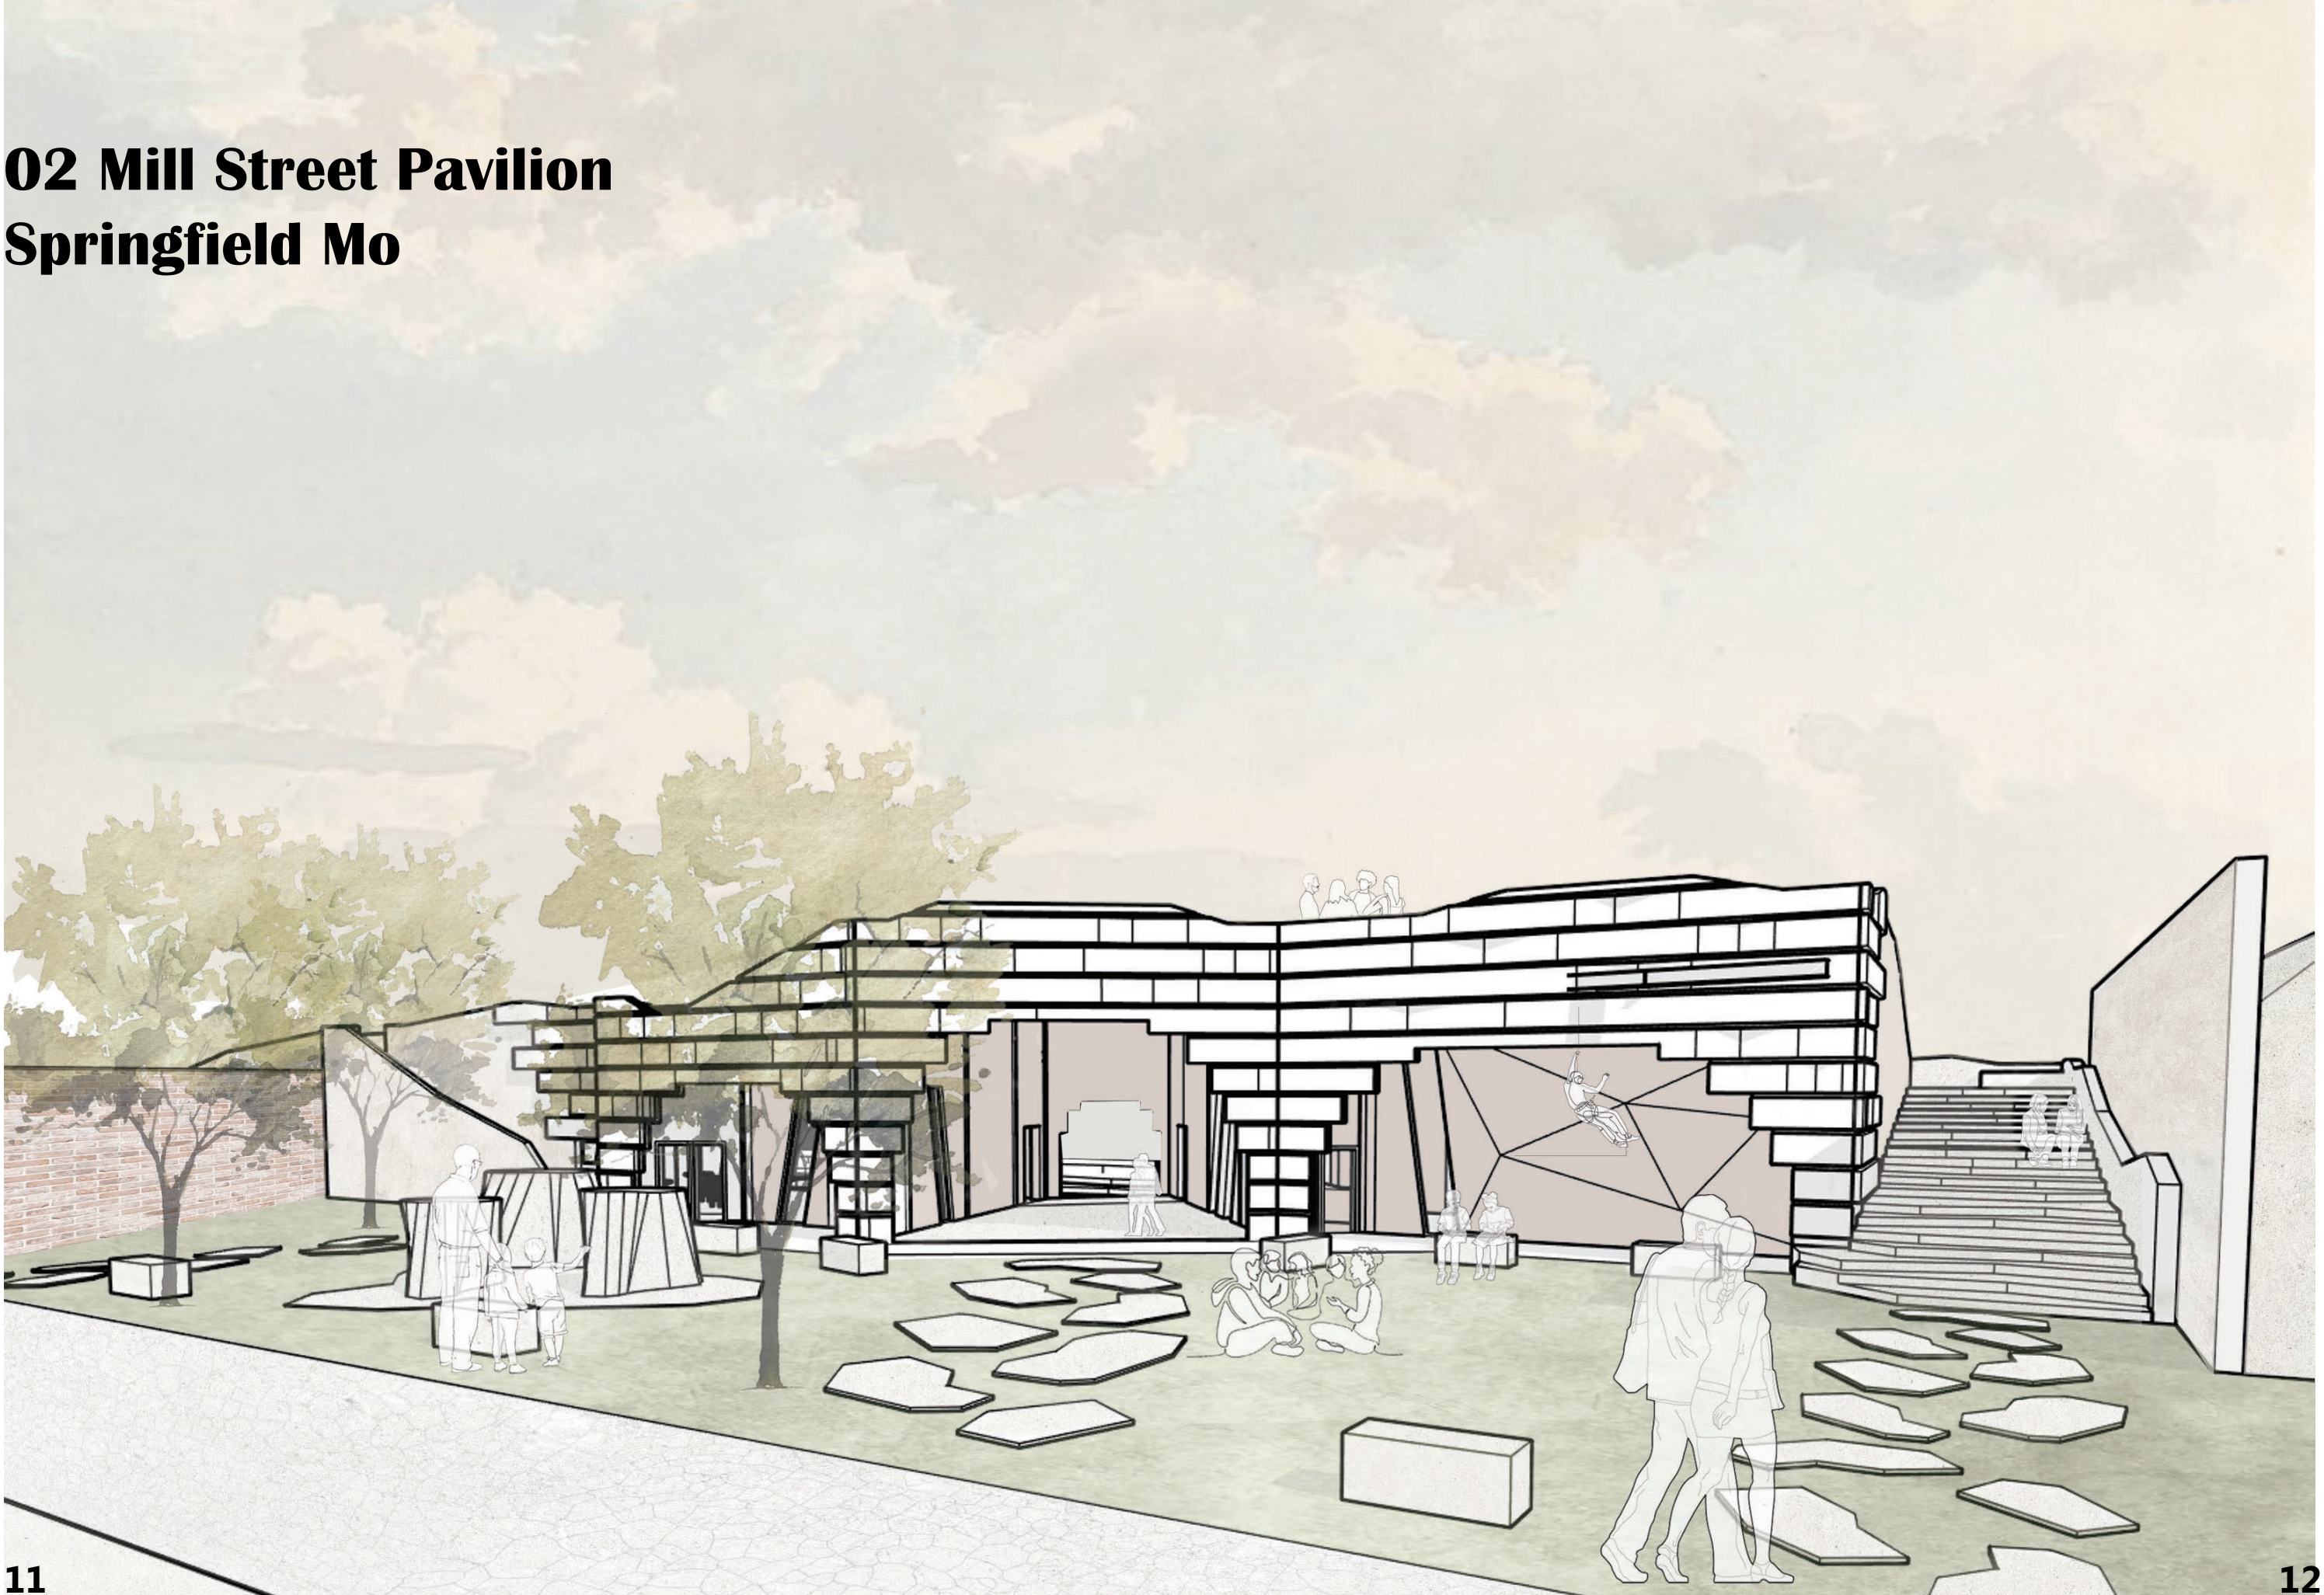


Pavilion and community space

Partner project
-Contribution: Design development
+ Diagrams + renderings + 50% of
the Physical model

The building is conceived as an abstract interpretation of Ozark vernacular architecture, drawing inspiration from the region’s mountainous landscape and outdoor culture. The design references activities commonly associated with the Ozarks such as bouldering, camping, and hiking to inform spatial organization and circulation. Rock climbing plays a central role in the project, directly influencing the floor plan by shaping vertical connections, program adjacencies, and the overall spatial experience.

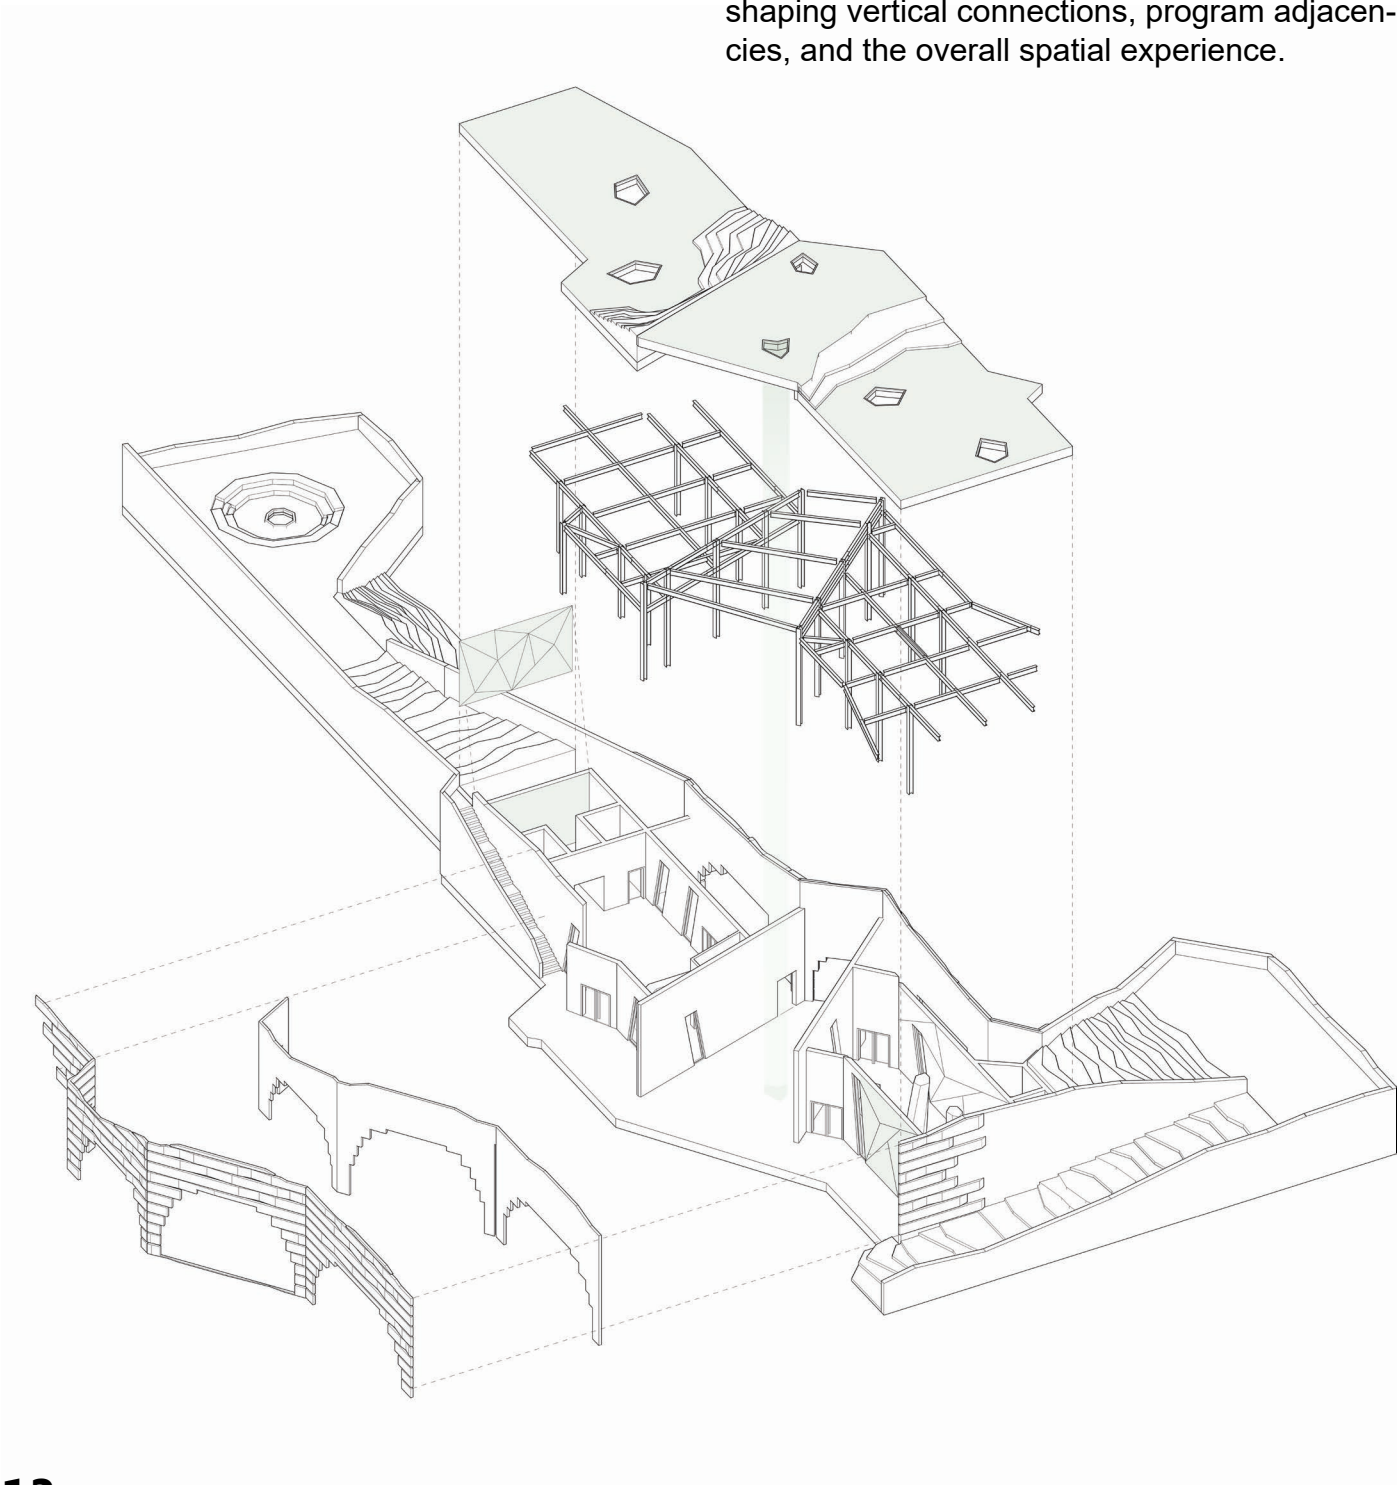

Form
The pavilion’s form is inspired by the Ozark vernacular, shaped by the topography of the region, bluffs, and cave structures to create spaces that reflect the character of the

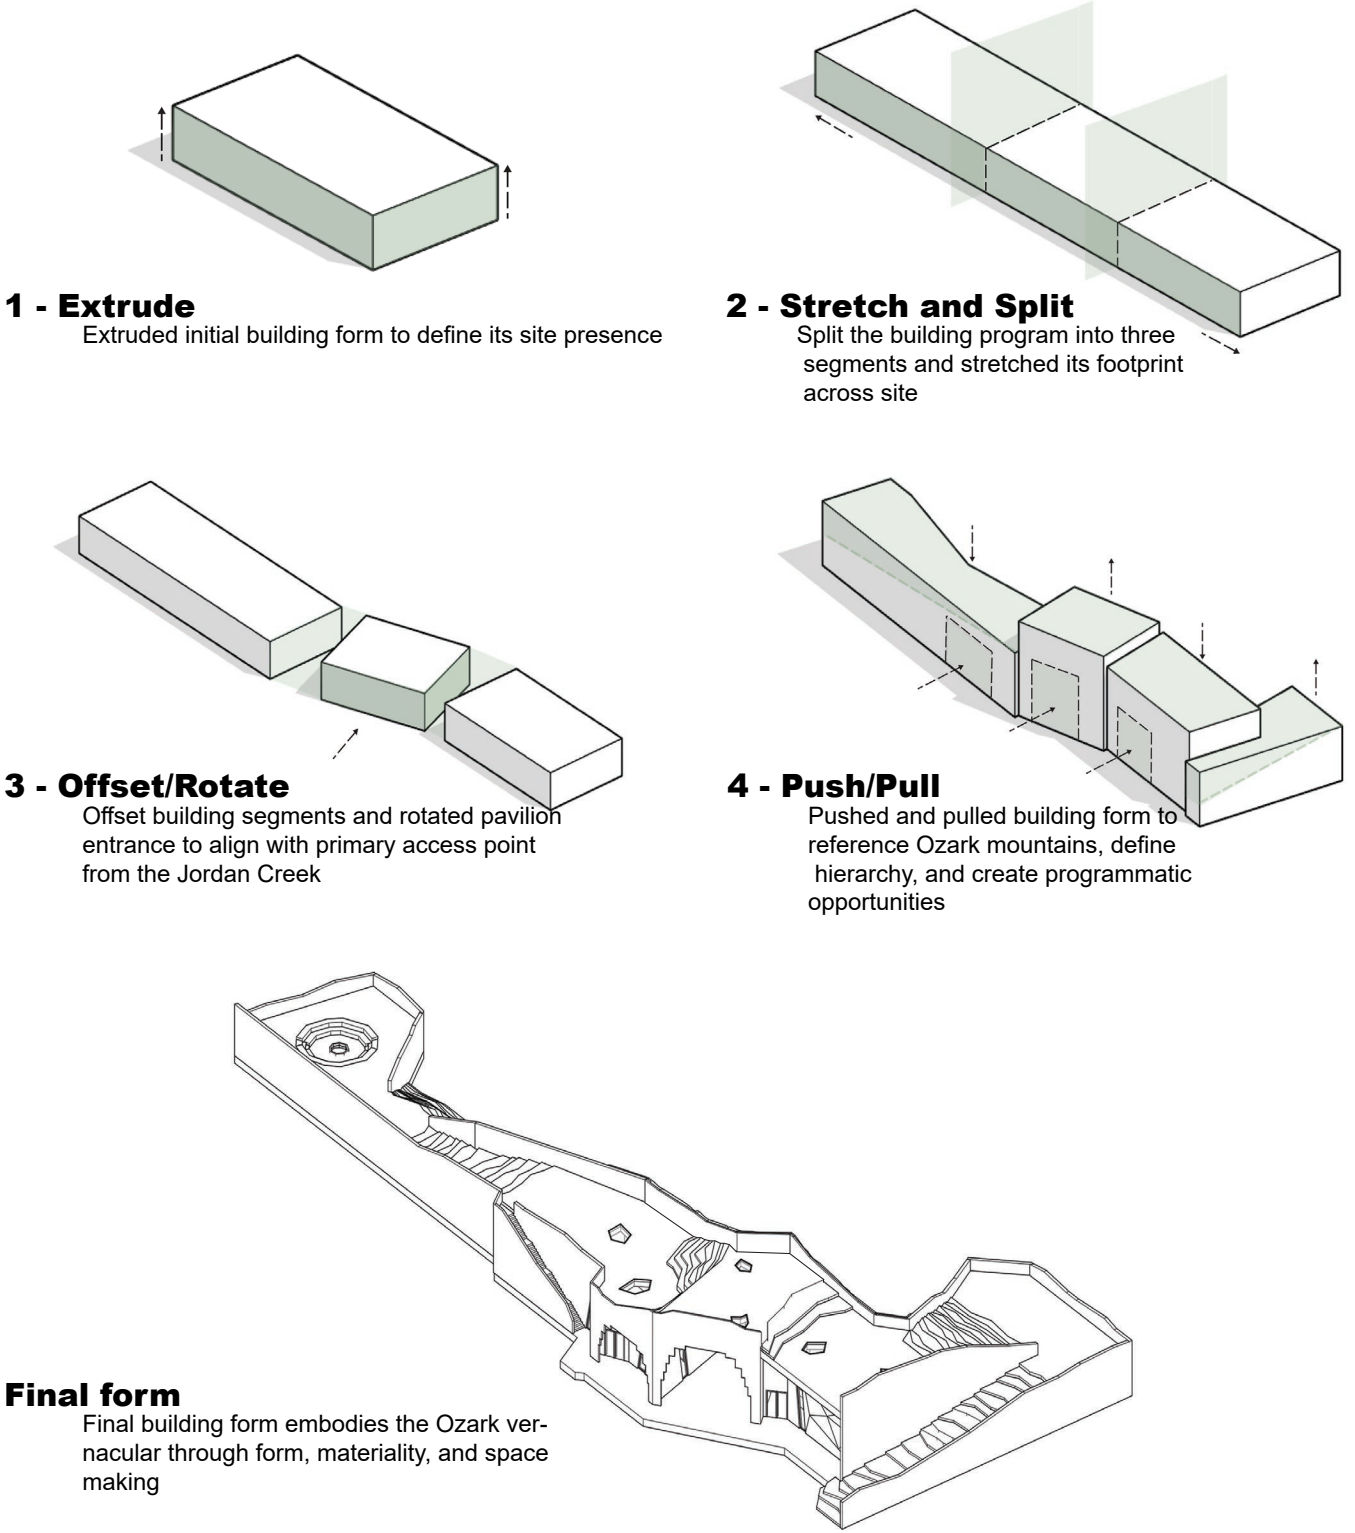



1 - Extrude
Extruded initial building form to define its site presence


2 - Stretch and Split
Split the building program into three segments and stretched its footprint across site

3 - Offset/Rotate
Offset building segments and rotated pavilion entrance to align with primary access point from the Jordan Creek

4 - Push/Pull
Pushed and pulled building form to reference Ozark mountains, define hierarchy, and create programmatic opportunities

Final form
Final building form embodies the Ozark vernacular through form, materiality, and space making

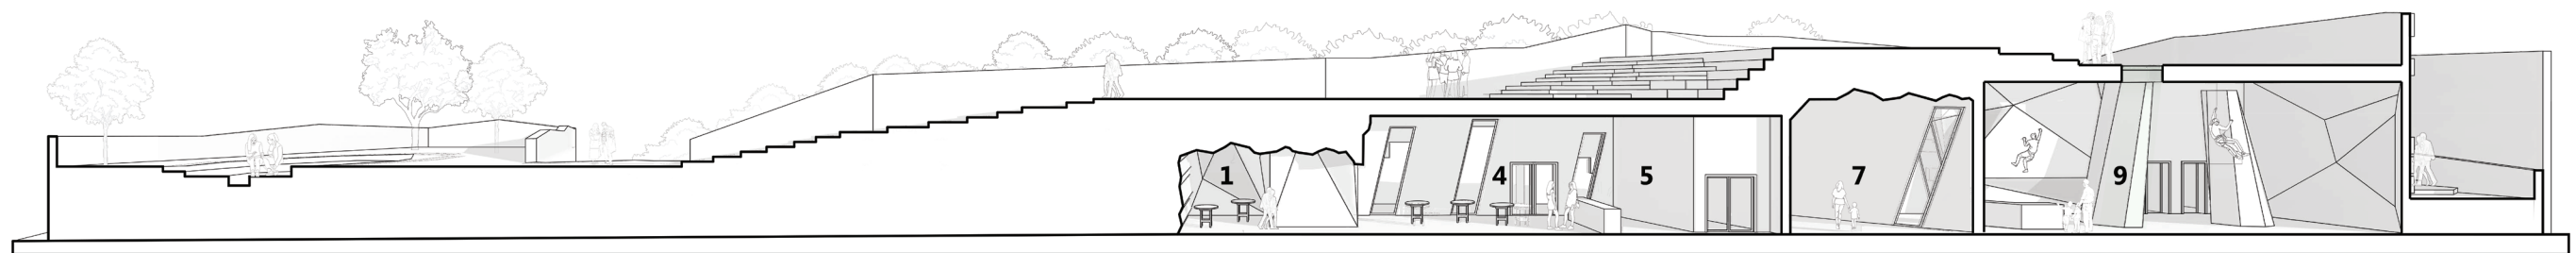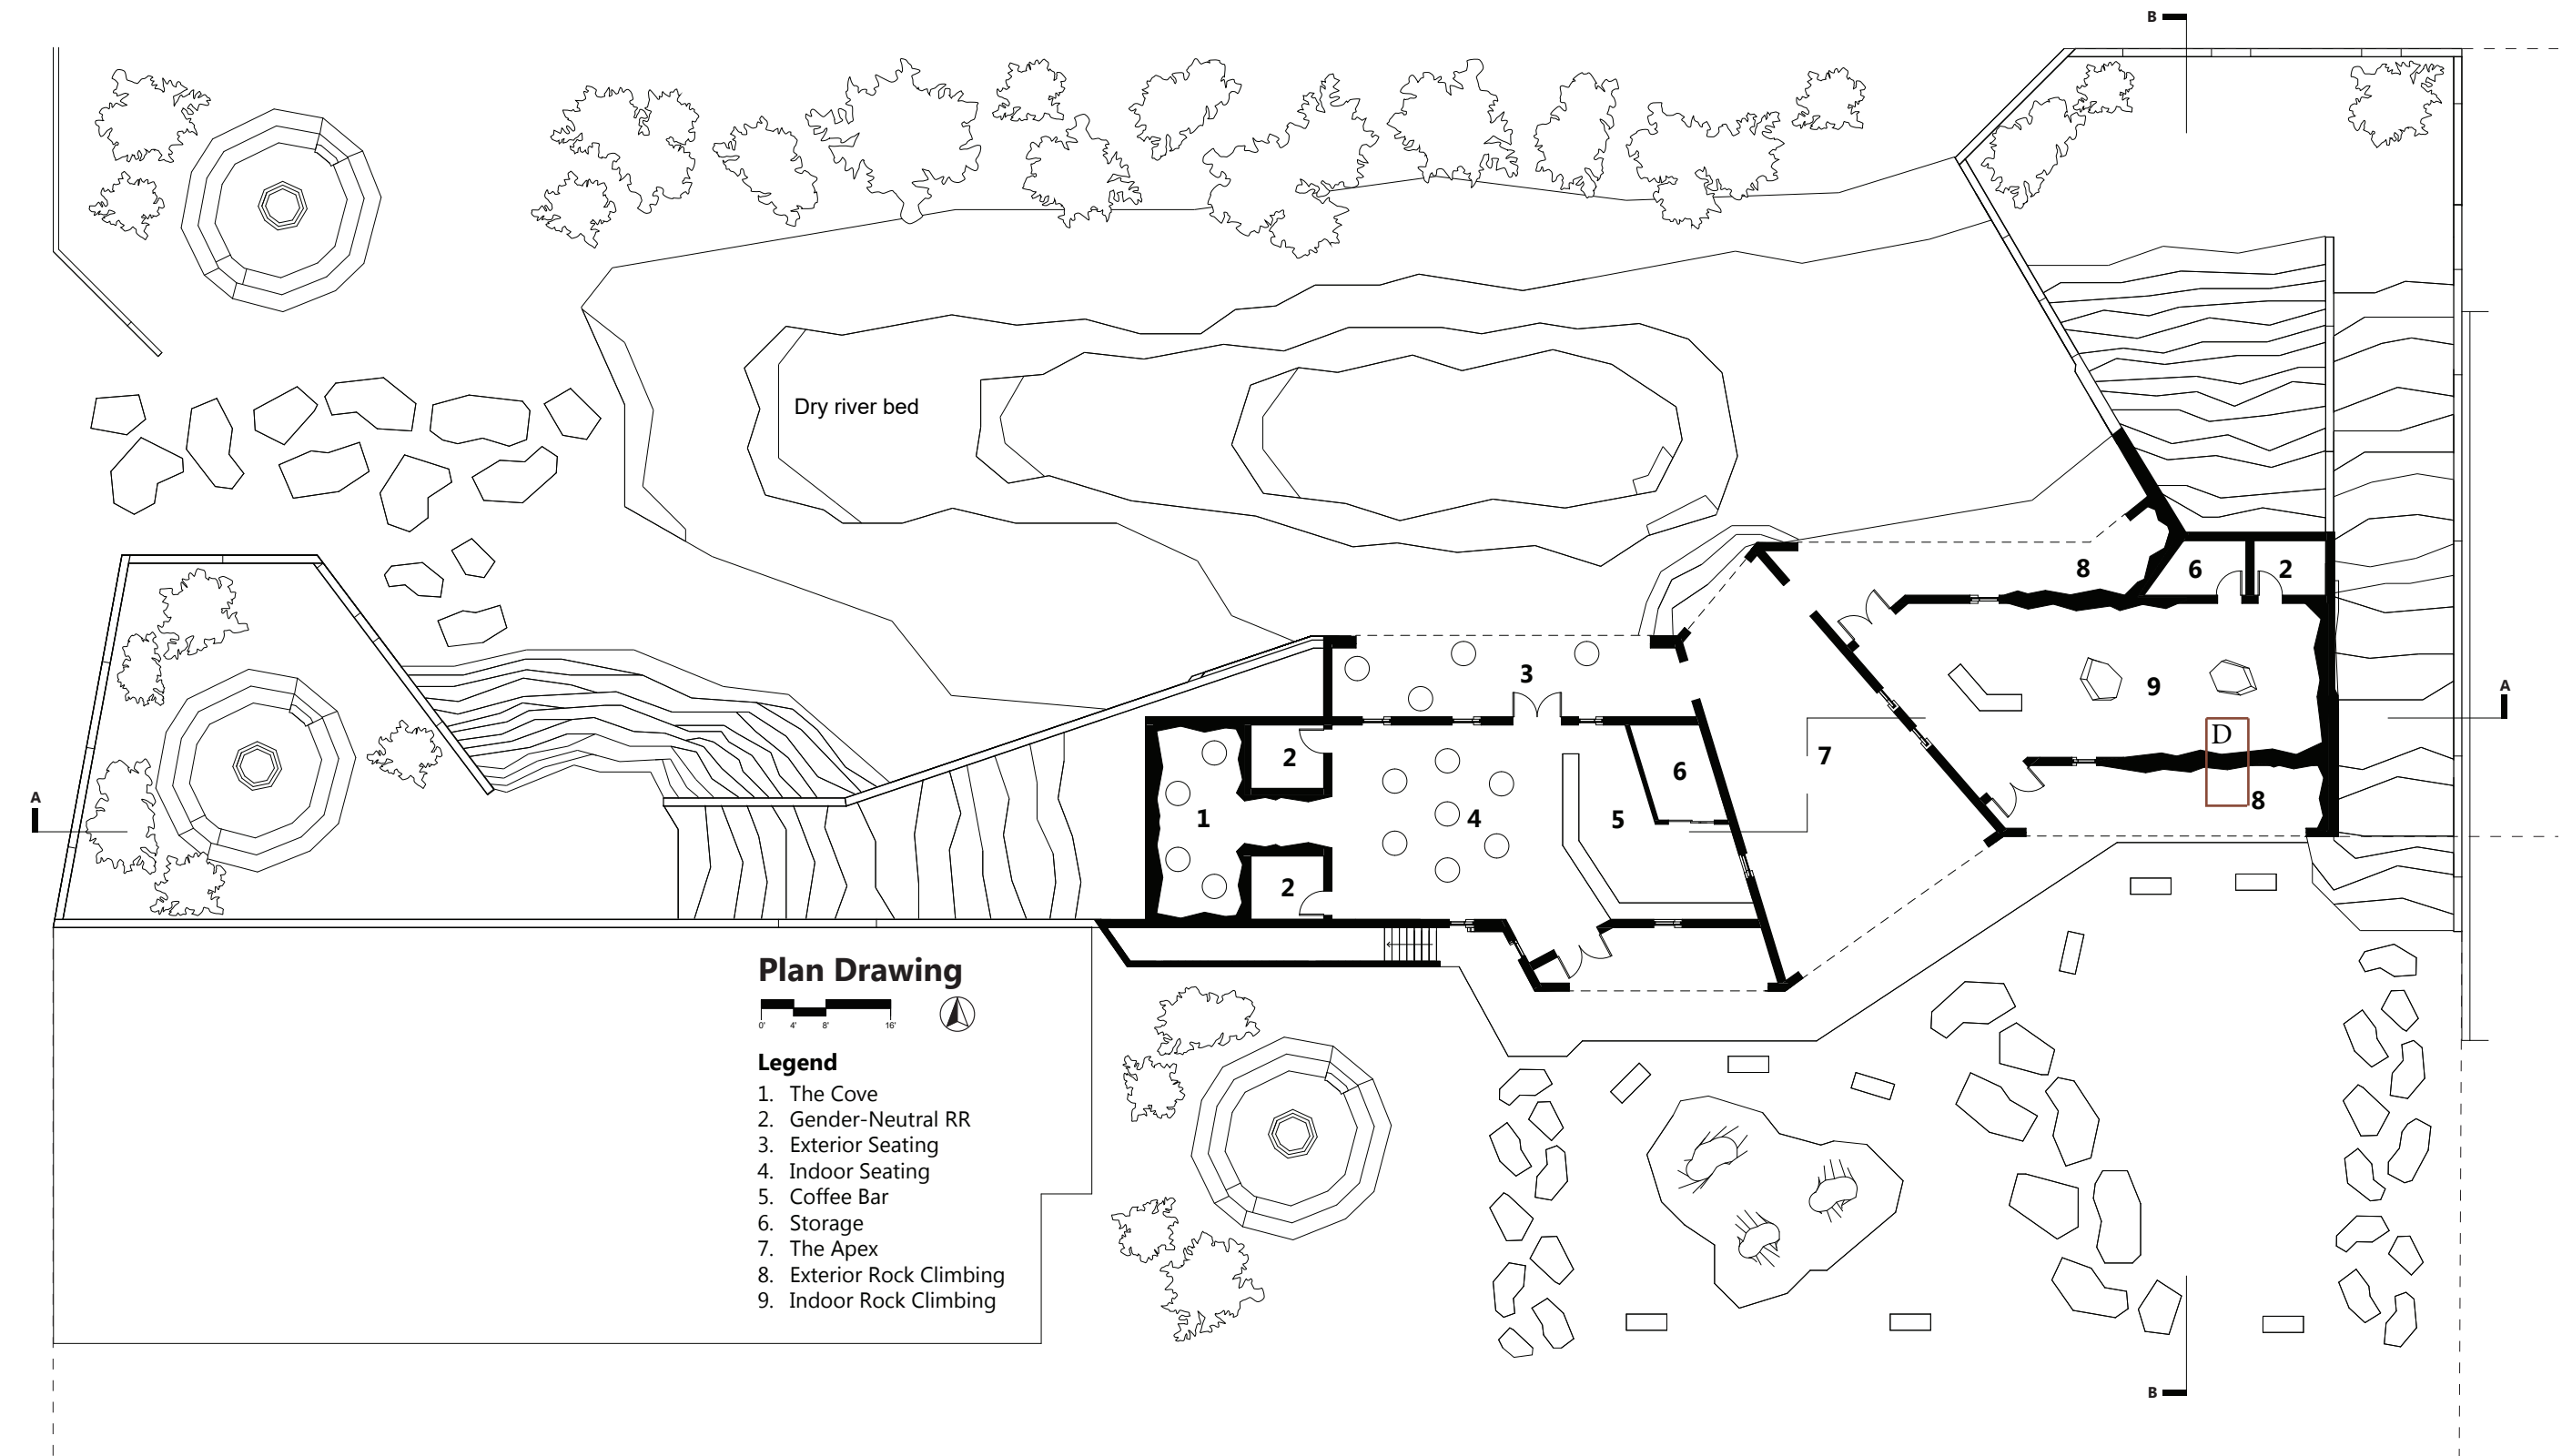

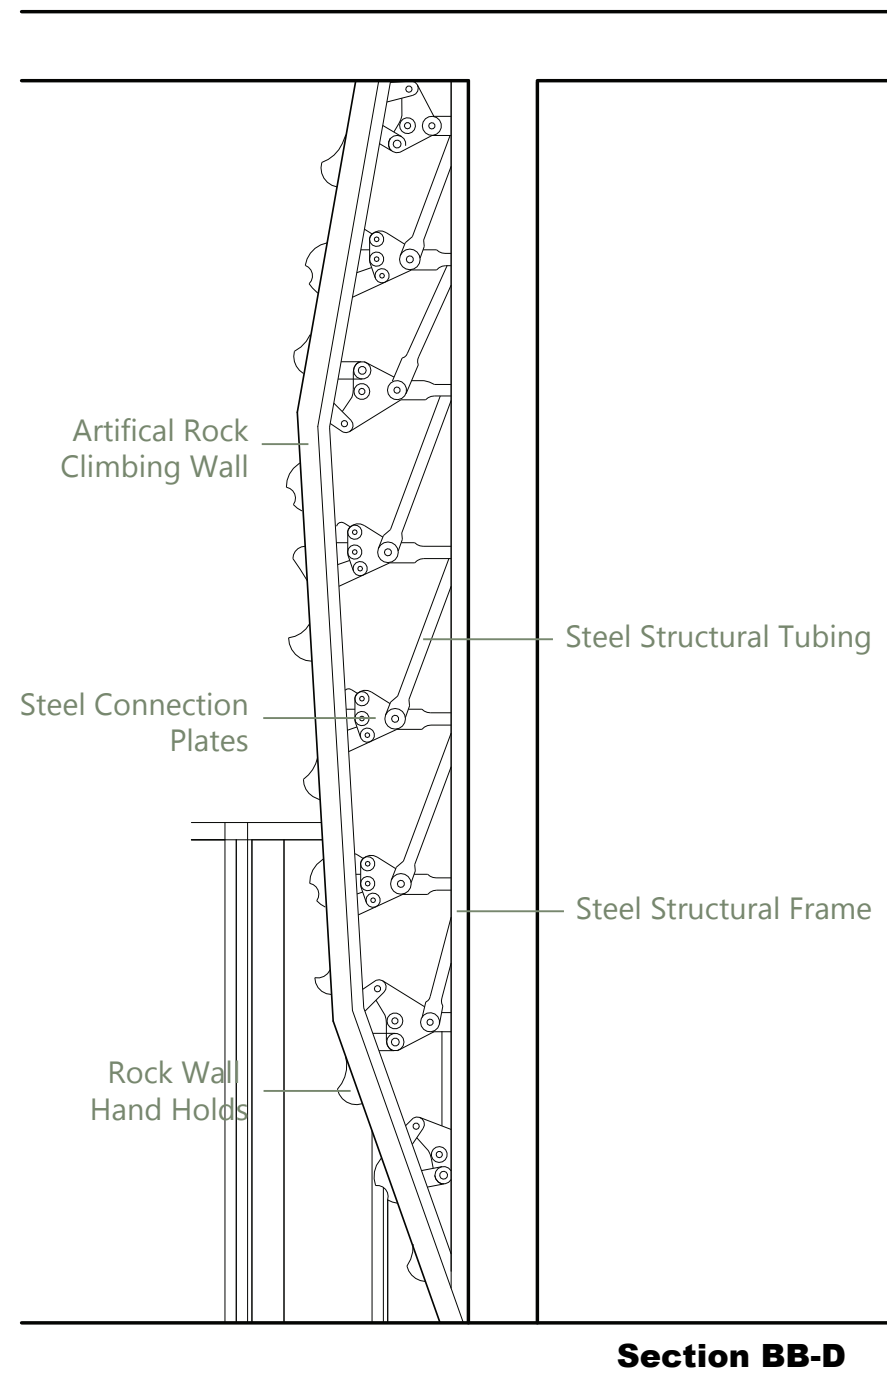

Technical Detail

Rock Climbing Wall



Coffee bar





Dry river bed

03-Modern Winery
Paris, France




Winery and verical farming


The form of the skyscraper is derived from the initial gesture of wine tasting the swirling of the glass before the acts of smelling and drinking. This motion becomes an archi-tectural generator, translating rotation and fluidity into the tower's massing. Inspired by the winemaking process, which is cyclical, labor-intensive, and repetitive yet yields a unique result each time, the building adopts a circular form with varying floor dimensions. These subtle inconsistencies reflect the evolving nature of wine production and create a dynamic vertical experience.

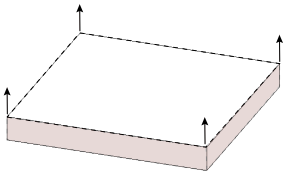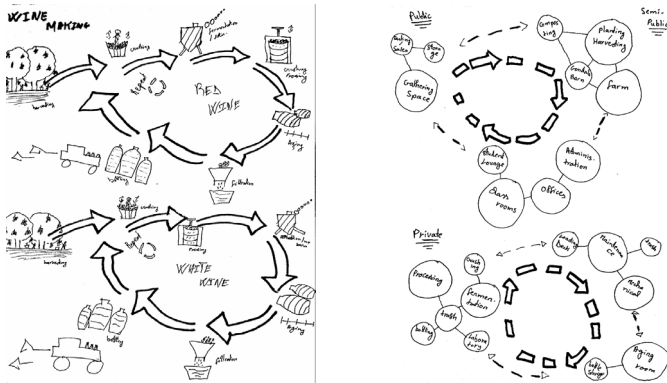


1-Extrude
Set building boundaries using the site footprint

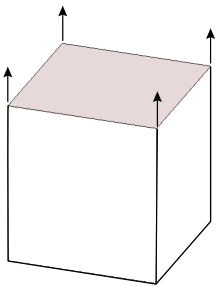


2-Stretch
Stretch building vertically

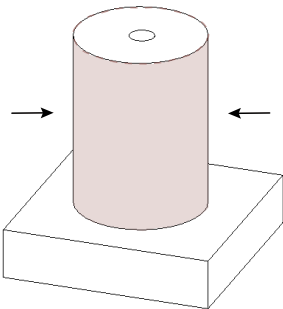


3-Change in form
Transitioning from a rectangular form to a circular form emphasizing the concept of rotation and repetition during the wine making process

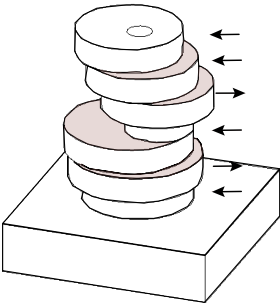


4-Offset
Offsetting Each floor for a more natural flow which derives from the swirling motion while wine tasting and resizing each floor depending on the program of the floor

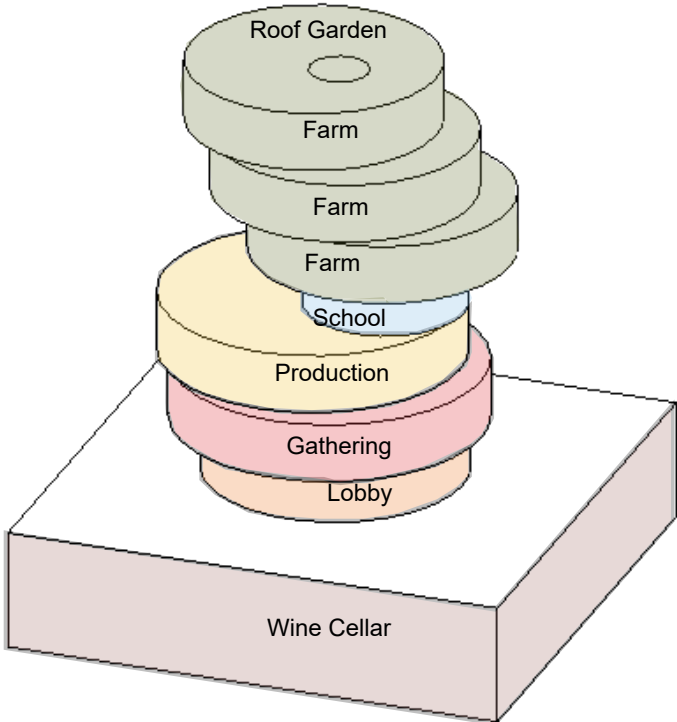


Section

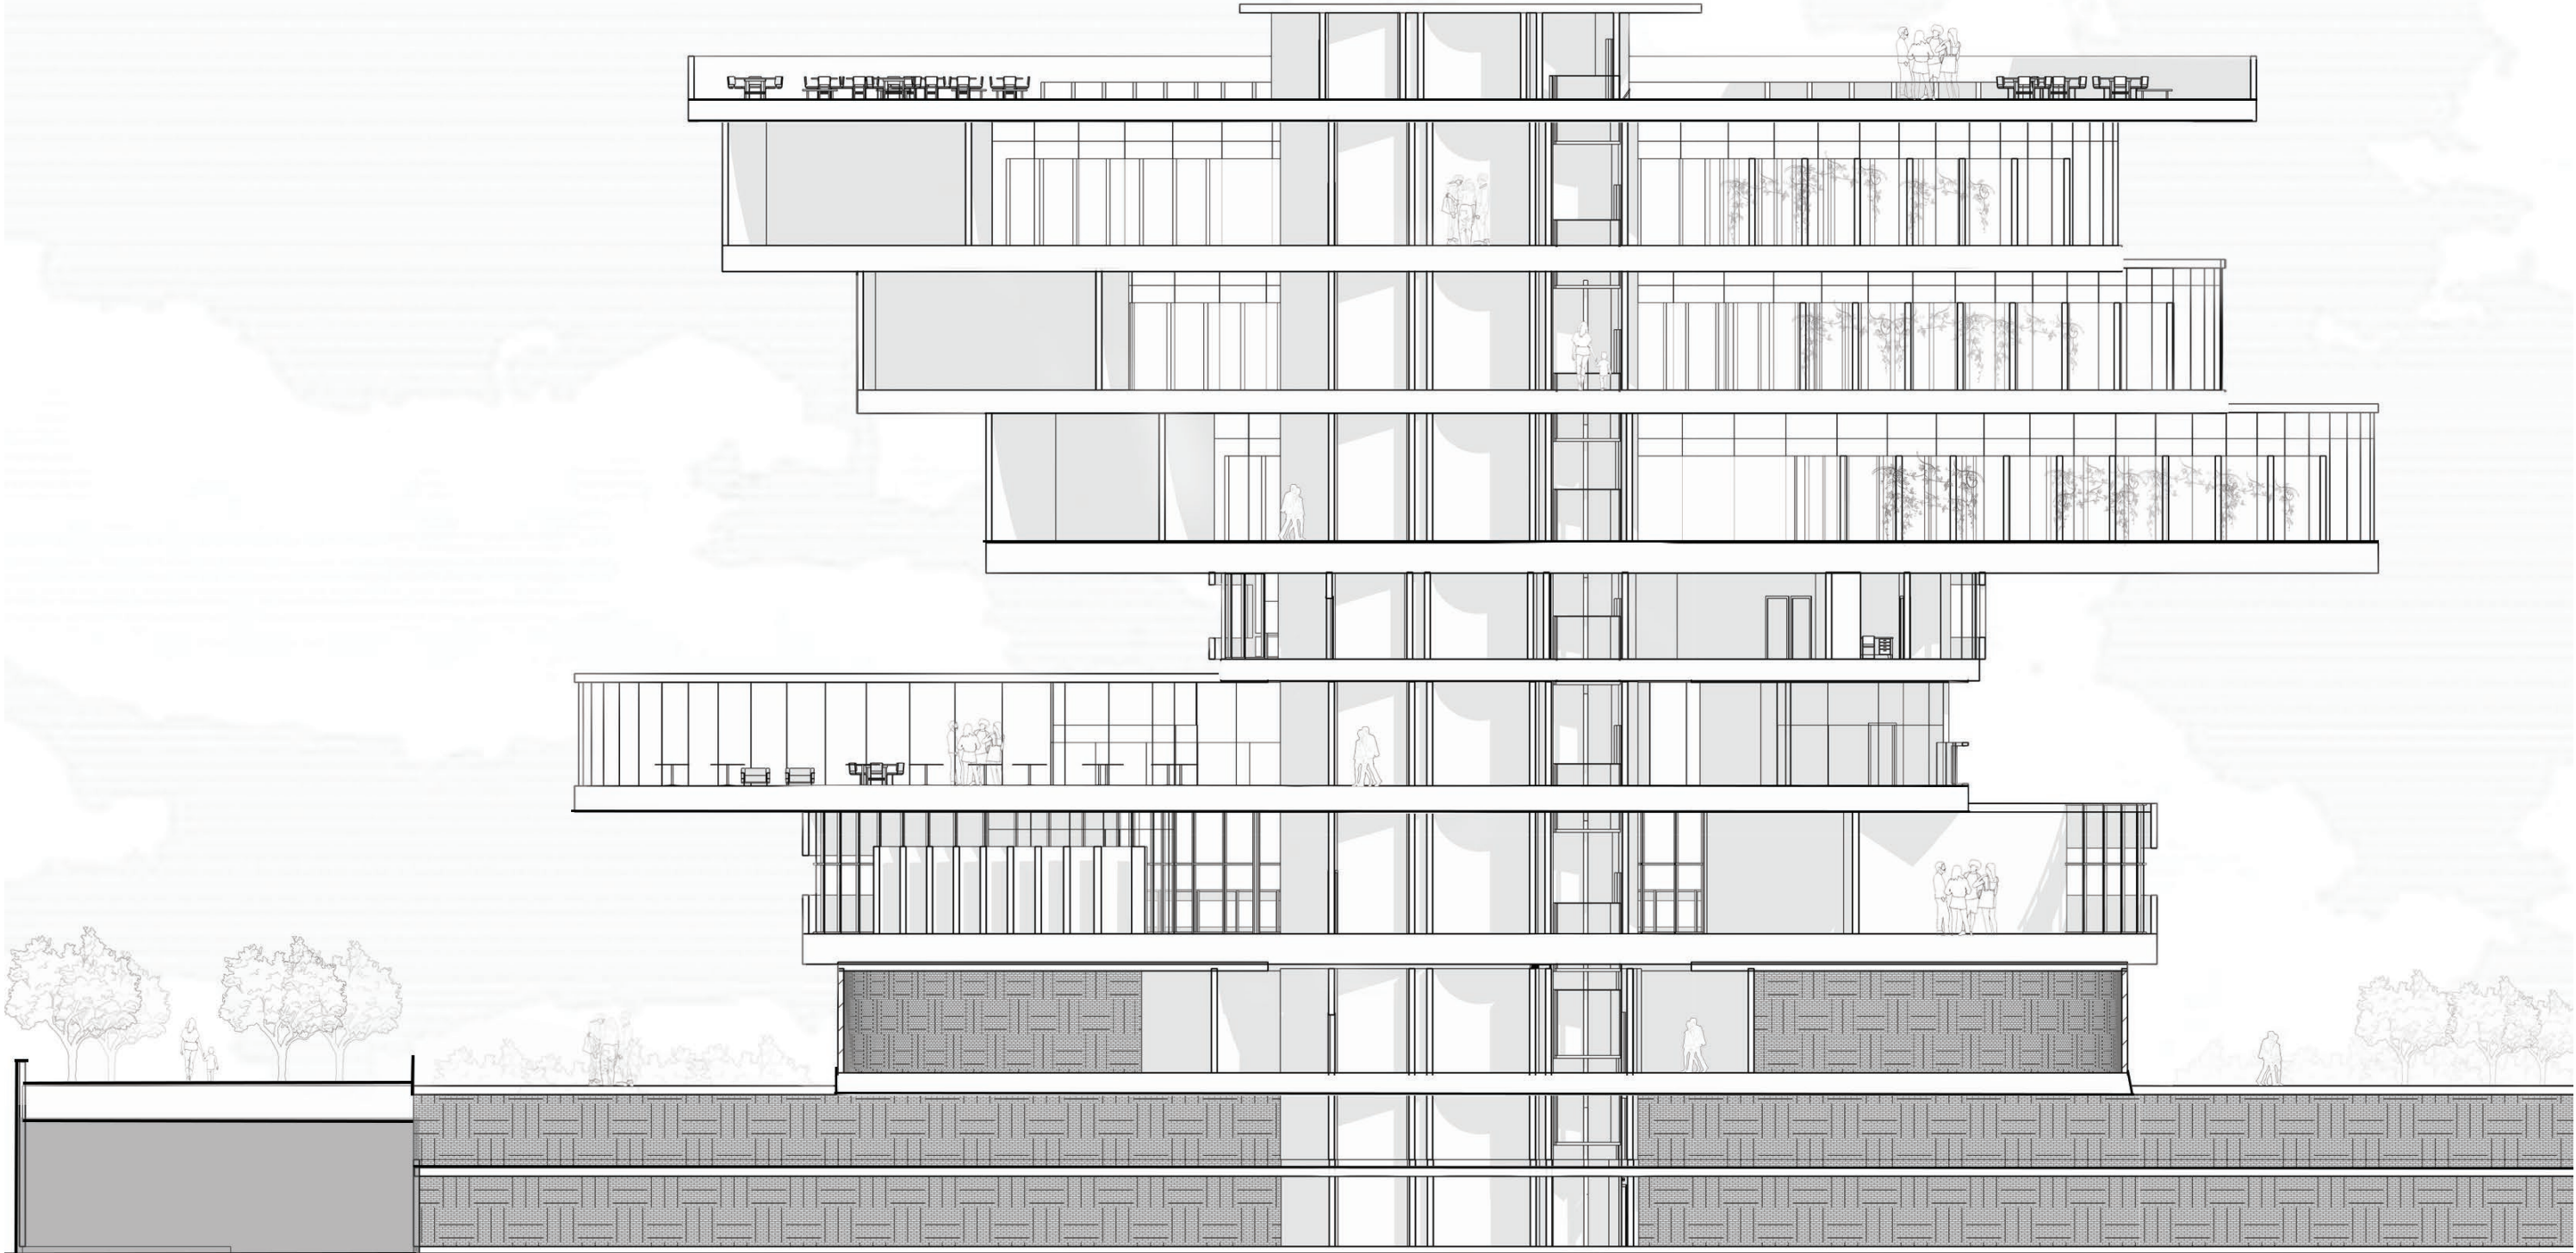


Model Making+Sketches

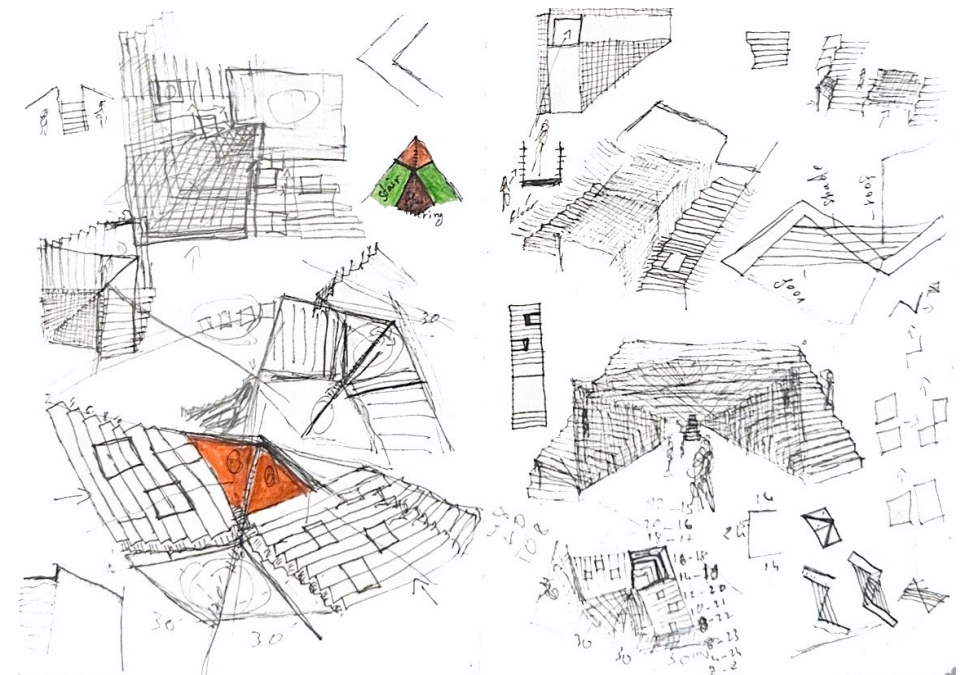

Travels+Photography

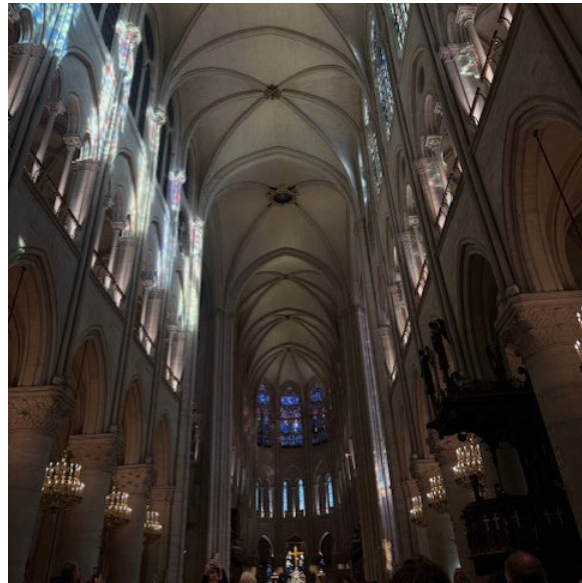

Paris, France

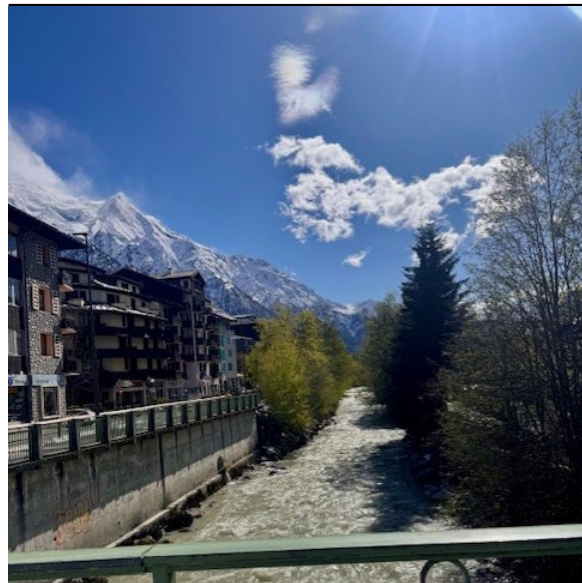

Mont-Blanc, Switzerland



Rome, Italy



Milan, Italy




Barcelona, Spain



London, UK



Dubai, UAE

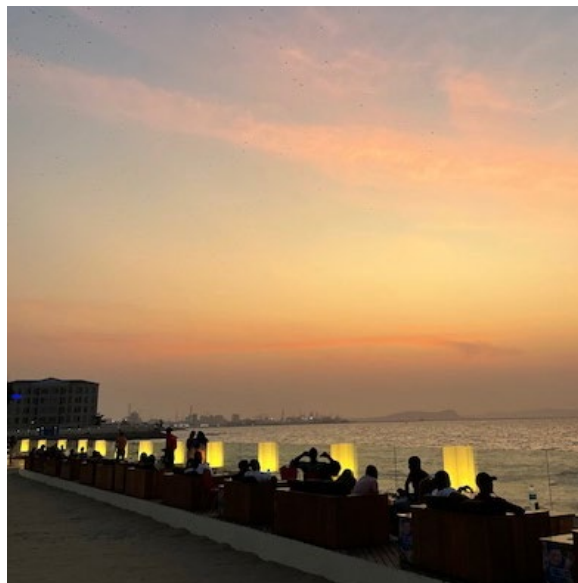

Guinea, West-Africa



Puerto rico, US



Us virgin islands, US

